
1 SITE PLAN SCALE: 1 : 400



2 GROUP PLAN SCALE: 1 : 200

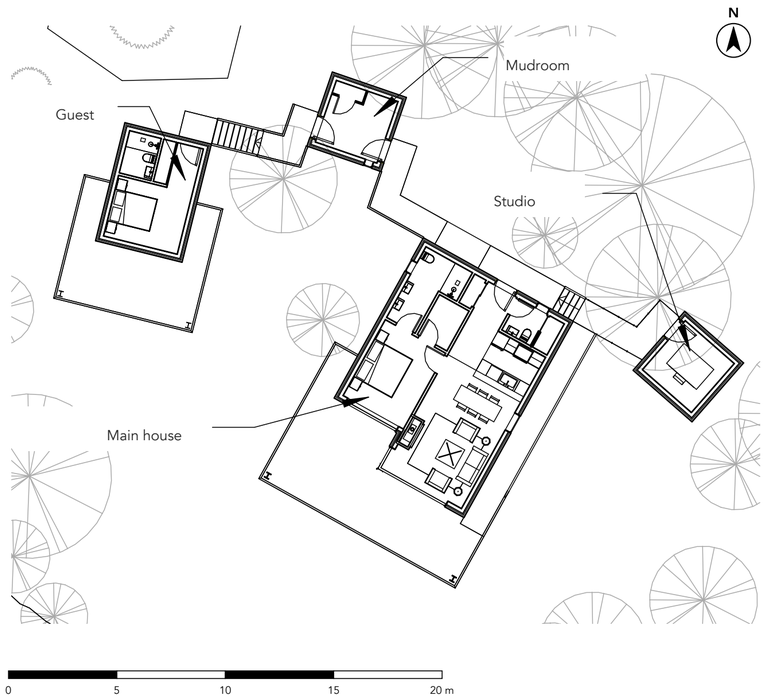

ROOM AREAS

	m²	ft²
Mudroom	**8**	**86**
Main house	**60**	**646**
Entry	6	65
Kitchen	5	54
Great Room	23	248
Powder Room	2	22
Laundry	1	11
Bedroom	13	140
Ensuite	7	75
Closet	3	32
Guest house	**16**	**172**
Guest Bedroom	13	140
Bathroom	3	32
Studio	**9**	**97**
Enclosed rooms	**93**	**1,001**

Net room areas are measured to the inside faces of the walls.
The roof-space storage (about 15 m², hatch access, mechanical) is excluded.
Gross area, to the outside of the walls, measured from the plans:
mudroom 13, main house 75, guest house 23, studio 13 m²,
about 124 m² in total (about 1,340 ft²).

North is up the sheet. The floor plans on sheet A-2 share this orientation.

MUSKOKA COTTAGE: THE TREEHOUSE


Site plan, group plan and room areas

Design Studio, Winter 2024 | Drawn by Steven Estafanos


SHEET A-1

SCALE As noted


1 MUDROOM PLAN SCALE: 1 : 75

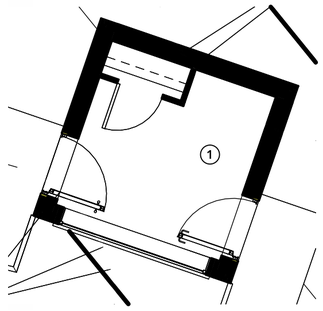


3 GUEST HOUSE PLAN SCALE: 1 : 75

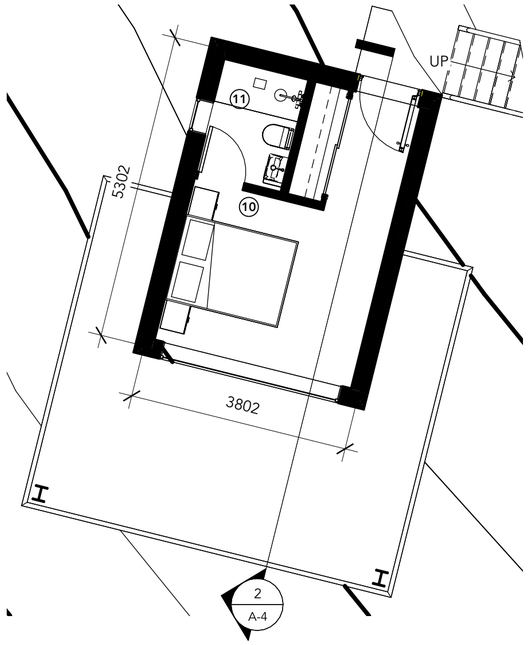

2 MAIN HOUSE PLAN SCALE: 1 : 75

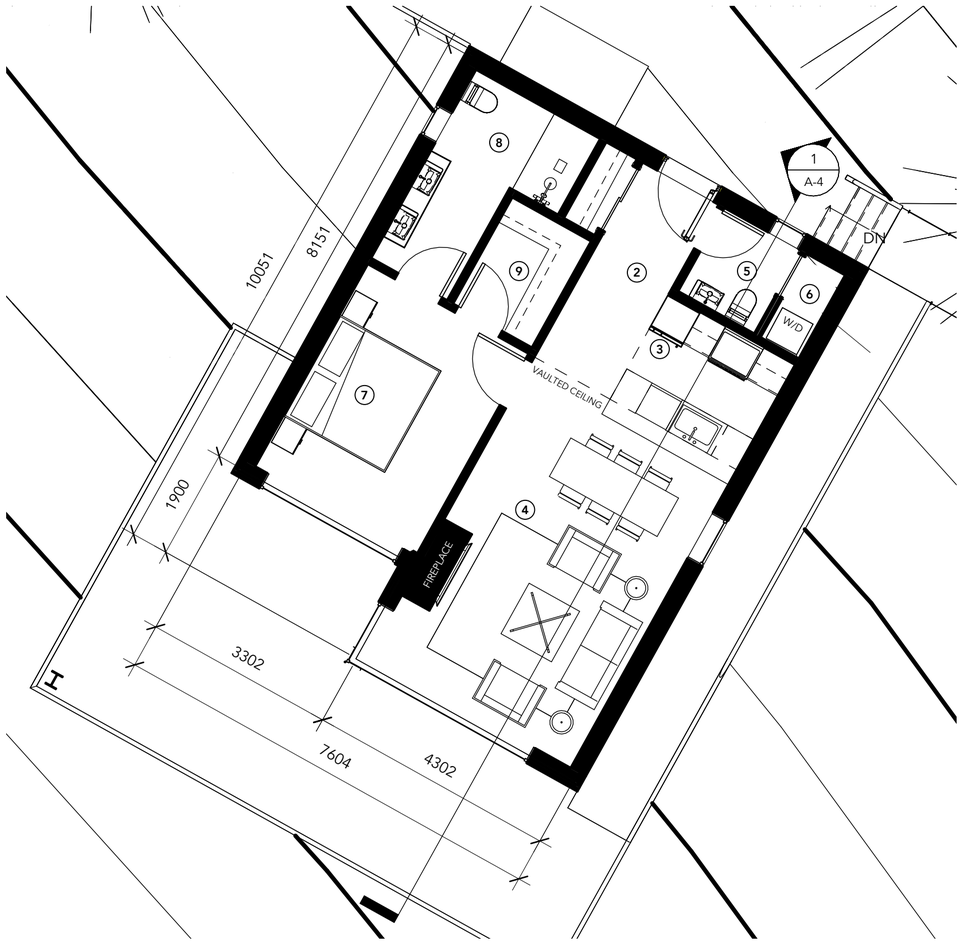

4 STUDIO PLAN SCALE: 1 : 75

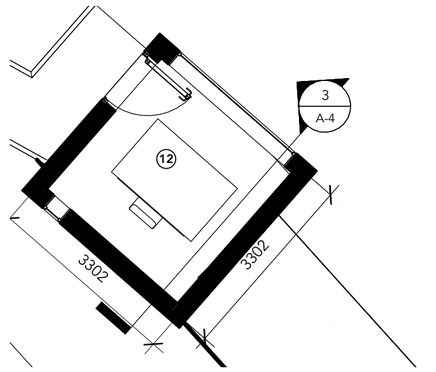

ROOMS

1. Mudroom
2. Entry
3. Kitchen
4. Great Room
5. Powder Room
6. Laundry
7. Bedroom
8. Ensuite
9. Closet
10. Guest Bedroom
11. Bathroom
12. Studio

N

0 1 2 3 4 5 m

Plans are placed as the buildings sit on the site (see the group plan, sheet A-1).

MUSKOKA COTTAGE: THE TREEHOUSE


Floor plans

Design Studio, Winter 2024 | Drawn by Steven Estafanos

SHEET **A-2**


SCALE 1 : 75

1 **"SOUTH" ELEVATION** SCALE: 1 : 75

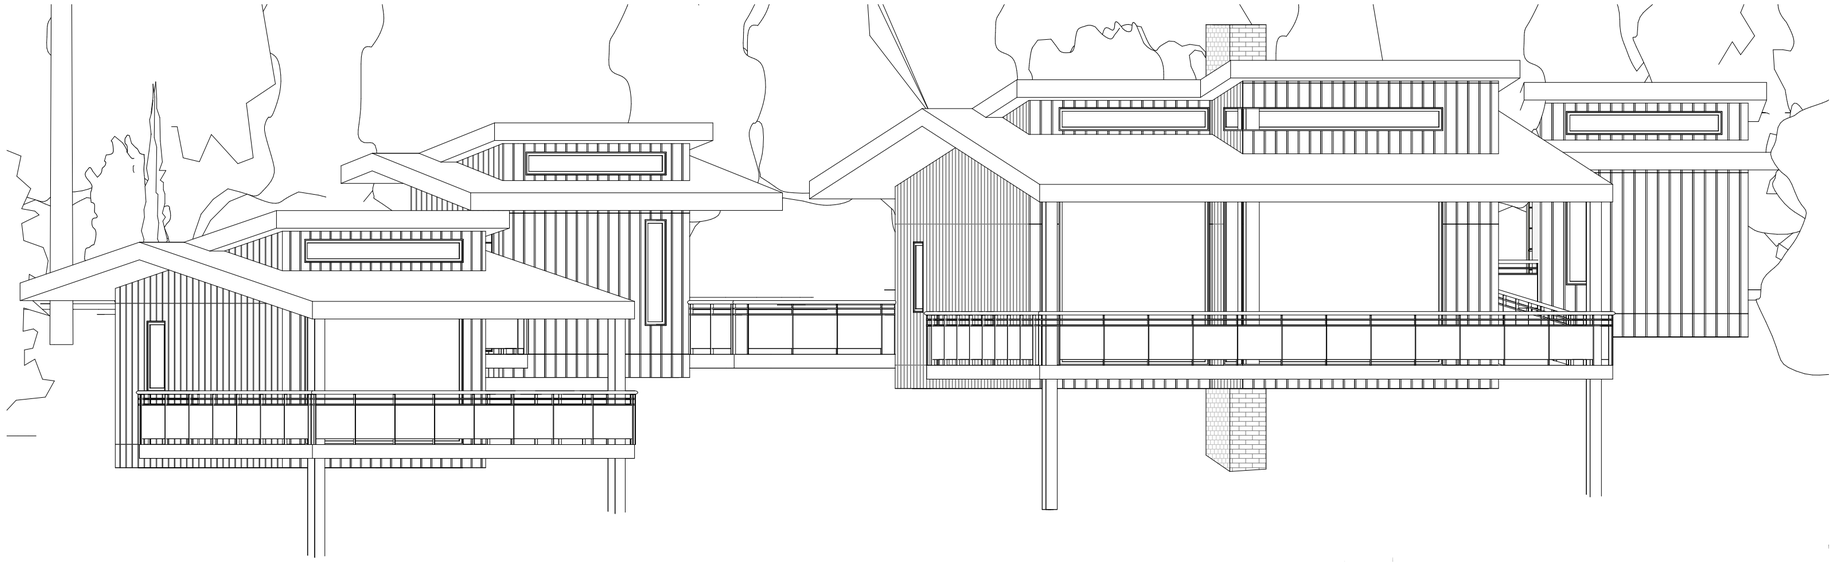

0 2 4 6 8 10 m

2 **"EAST" ELEVATION** SCALE: 1 : 75

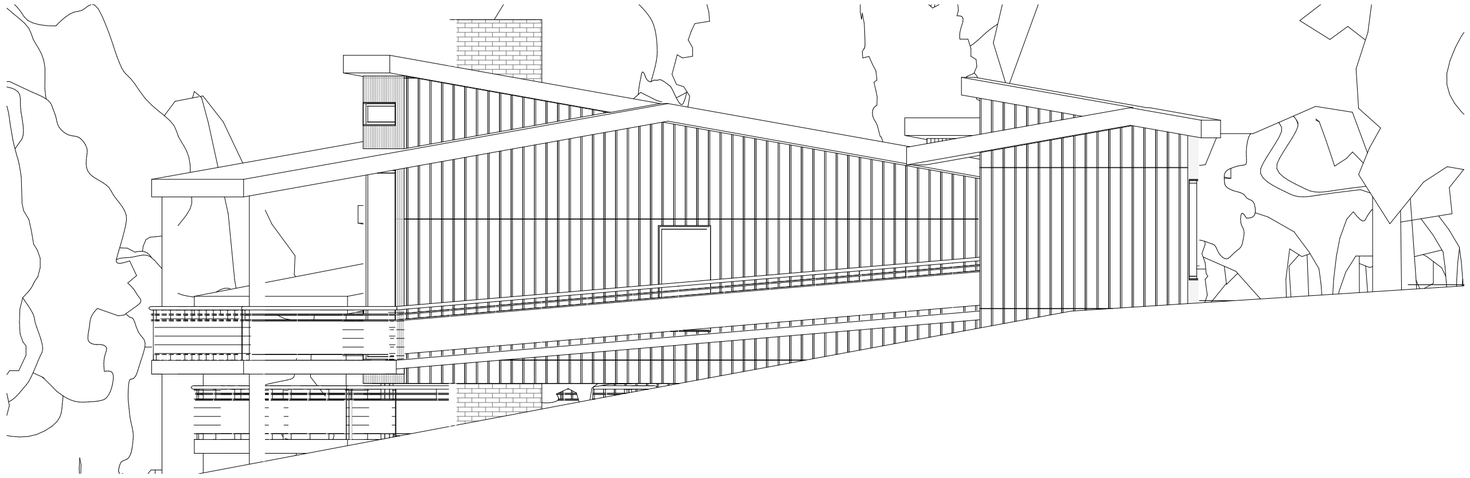

0 2 4 6 8 10 m

MUSKOKA COTTAGE: THE TREEHOUSE


South and east elevations

Design Studio, Winter 2024 | Drawn by Steven Estafanos

SHEET **A-3**


SCALE 1 : 75

1 MAIN HOUSE SECTION SCALE: 1 : 75

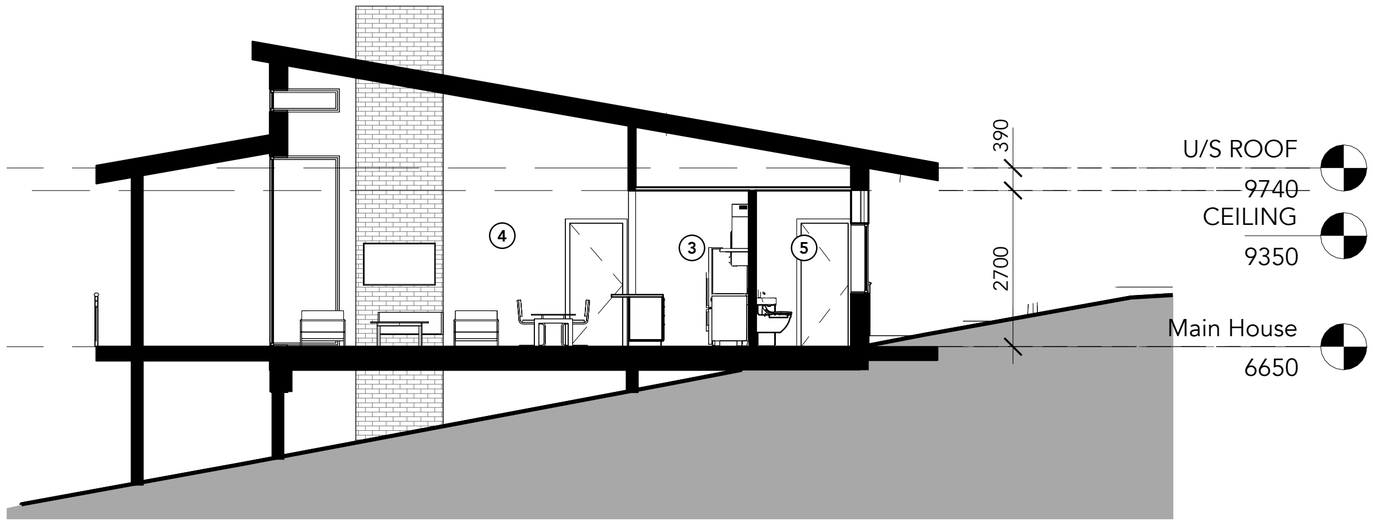




2 GUEST HOUSE SECTION SCALE: 1 : 75

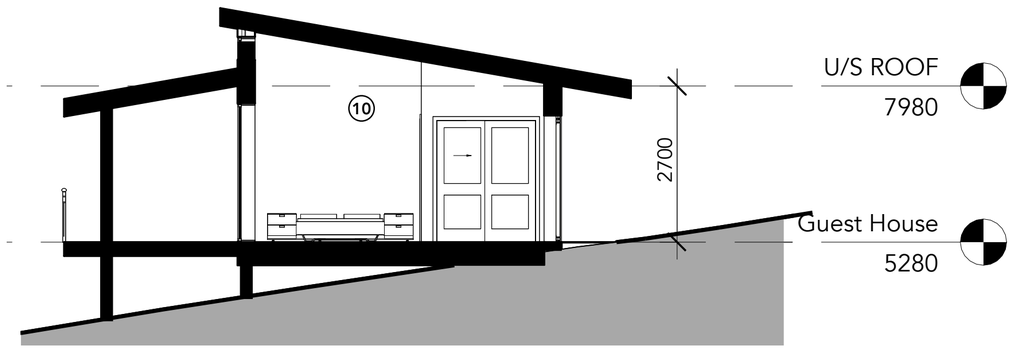

3 STUDIO SECTION SCALE: 1 : 75

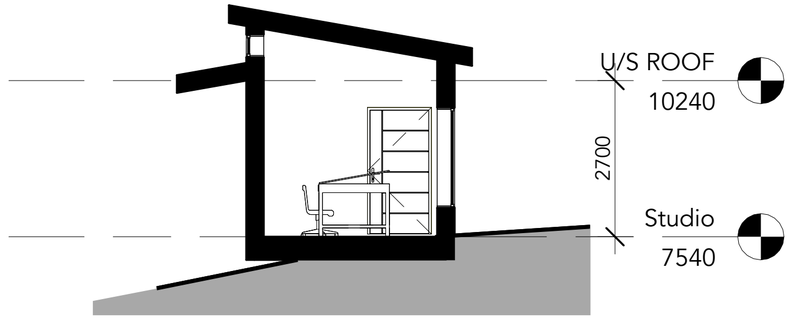



Levels are in millimetres.

MUSKOKA COTTAGE: THE TREEHOUSE

Sections

Design Studio, Winter 2024 | Drawn by Steven Estafanos

SHEET **A-4**

SCALE 1 : 75