PROJECT & BUILDING STATISTICS:


BUILDING HEIGHT:	23'-0"
BUILDING AREA:	
BASEMENT:	856 SQ FT
GROUND FLOOR:	879 SQ FT
TOTAL GROSS AREA:	879 SQ FT
TOTAL FOOTPRINT:	879 SQ FT

SB-12 CALCULATION SUMMARY:

OBC COMPLIANCE PACKAGE A1
SB-12, TABLE 3.1.1.2.A (IP)

DRAWING INDEX:

A0.0 COVER
A0.1 GENERAL NOTES
A0.2 WINDOW SCHEDULE DOOR SCHEDULE
A1.1 SITE/GRADING PLAN
A2.1 BASEMENT PLAN
A2.2 FIRST FLOOR PLAN
A4.1 FRONT ELEVATION
A4.2 RIGHT SIDE ELEVATION
A5.1 BUILDING SECTION
A6.1 INTERIOR ELEVATION, KITCHEN
A7.1 SILL DETAILS
A7.4 EAVE DETAIL
A7.5 STAIR DETAILS

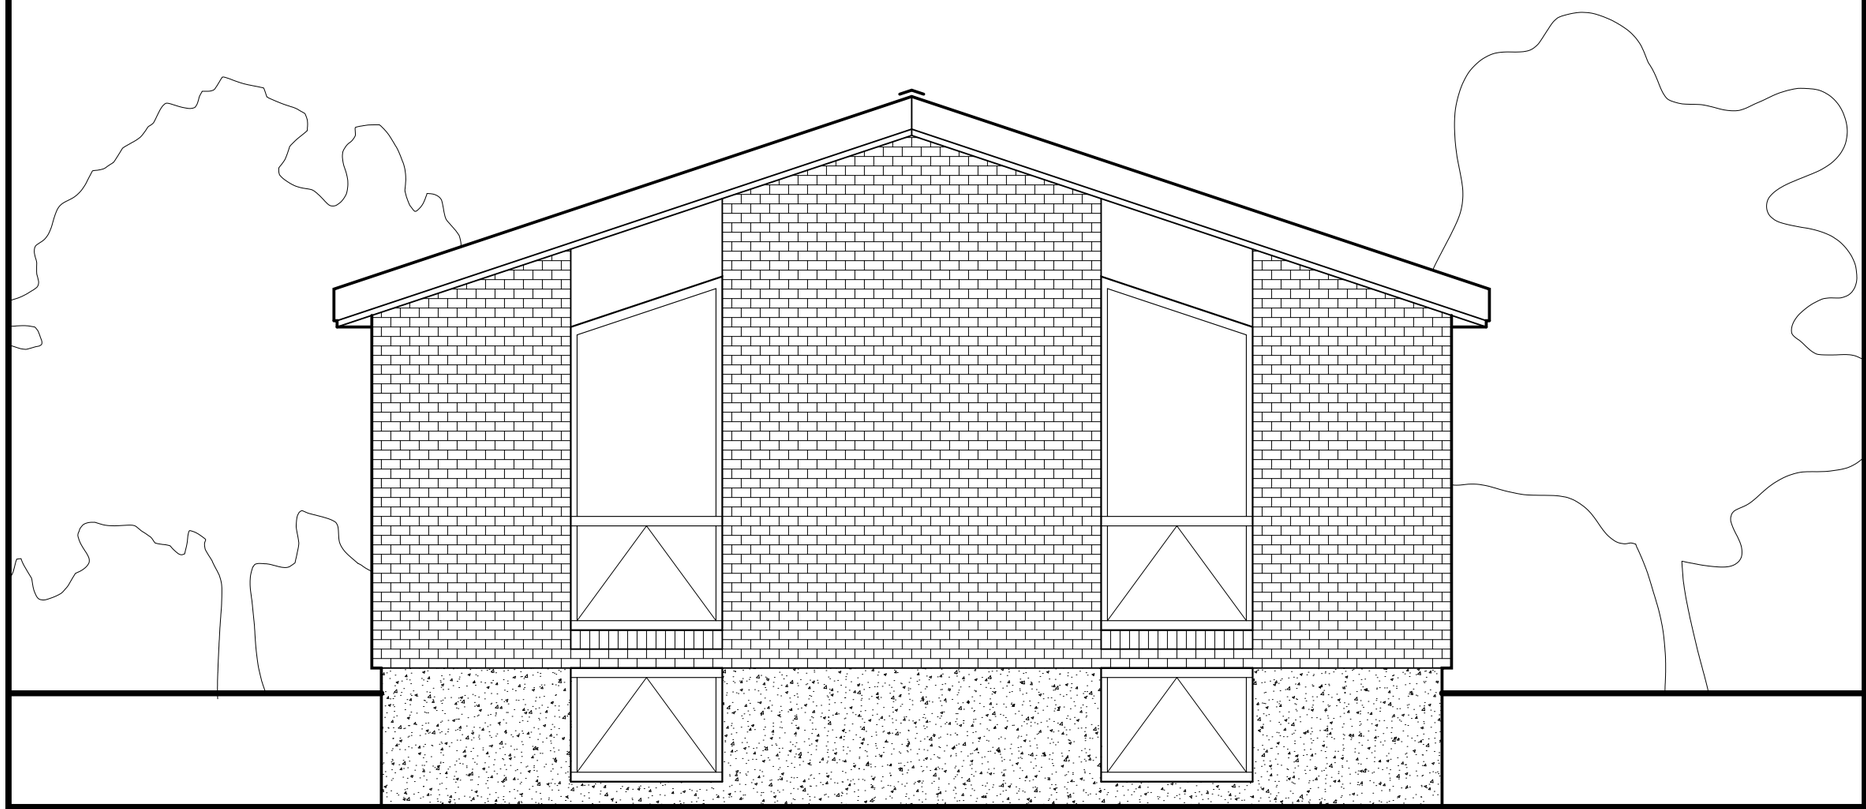

ESTAFANOS HOUSE

3421 LOCH NESS DRIVE, NESSAU, LC
N35 51E

NOTES

1. DO NOT SCALE DRAWINGS. USE FIGURED DIMENSIONS ONLY.

2. ALL WORK MUST MEET OR EXCEED THE ONTARIO BUILDING CODE'S LATEST EDITION AND ALL OTHER APPLICABLE CODES AND STANDARDS. WHERE CONFLICT OCCURS, THE HIGHER STANDARD GOVERNS.

3. THE CONTRACTOR IS RESPONSIBLE FOR TAKING AND CHECKING DIMENSIONS ON SITE. REPORT DISCREPANCIES TO THE ARCHITECT BEFORE COMMENCING ANY WORK.

NO	REVISION	DATE
1	FINAL SUBMISSION	12 APRIL 2023

PROJECT TITLE
ESTAFANOS HOUSE

DRAWING TITLE
COVER

NAME:	STEVEN ESTAFANOS
DATE:	12 APRIL 2023
CLASS:	ARC8401-020
SCALE:	NONE

A0.0

CONSTRUCTION ASSEMBLIES:

W1
1X6 VERTICAL CEDAR SIDING
1X4 DIAGONAL STRAPPING @16" O/C
1.5" CLADMATE RIGID INSULATION BOARD C/W
DIAGONAL METAL BRACING
2X6 STUDS@16" OC
R24 BATT INSULATION
POLY. AIR/VAPOUR BARRIER

W2
DRAINAGE LAYER
DAMPROOFING
8" P.I.P. CONC. FOUNDATION
INT. DAMPROOFING FROM GRADE LEVEL DOWN
1" AIR SPACE

W3
BRICK VENEER
1" AIR SPACE
1.5" CLADMATE INSULATION BOARD C/W
DIAGONAL METAL BRACING
2X6 STUDS @16" O/C
R-24 BATT INSULATION
POLY. AIR/VAPOUR BARRIER
1/2" GYPSUM BOARD

W4
SAME AS W2 EXCEPT
10" P.I.P. CONC. FOUNDATION

W5
1/2" GYPSUM BOARD
2x4 STUDS @ 16" O/C
1/2" GYPSUM BOARD

F1
FINISHED FLOORING (SEE PLANS)
- HWD-MAPLE HARDWOOD
- CT-CERAMIC C/W 5/8" OSB UNDERLAY

5/8" PLYWOOD T&G SUBFLOOR
2X10 FLOOR JOIST @16" O/C
STRUCTURAL SELECT
2 ROWS CROSS BRIDGING

F2
3" CONCRETE SLAB
8" COARSE GRANULAR
UNDISTURBED SOIL

R1
ASPHALT SHINGLES
EAVE PROTECTION
NO-15 FELT UNDERLAY
7/16" OSB SHEATHING C/W H-CLIPS
2X2 PURLINS @ 16" O/C
2X12 ROOF JOISTS@24" O/C. SELECT
R-32 BATT INSULATION
POLY. AIR/VAPOUR BARRIER
1x4 STRAPPING@16" O/C
1/2" GYPSUM BOARD

R2
ASPHALT SHINGLES
EAVE PROTECTION
NO-15 FELT UNDERLAY
7/16" OSB SHEATHING C/W H-CLIPS
2x10 RAFTERS@24" O/C, SELECT
2x8 CEILING JOISTS@24" O/C, SELECT
R-32 BATT INSULATION@RIGHT ANGLE TO CEILING JOISTS
R-28 BATT INSULATION IN CEILING JOIST
POLY. AIR/VAPOUR BARRIER
1X4 STRAPPING@16" O/C
1/2" GYPSUM BOARD

ELECTRICAL NOTES:

1. PROVIDE INTERCONNECTED SMOKE ALARMS AND C.O DETECTORS



2. LIGHT STAIRWELLS/W3 WAY SWITCHES, TOP & BOTTOM
3. PROVIDE LIGHTS@ EXTERIOR DOORS

NOTES:

1. ALL WORKS IN COMPLIANCE WITH O.B.C., LATEST RENDITION
2. DO NOT SCALE DRAWINGS

NO	REVISION	DATE
1	FINAL SUBMISSION	12 APR 2023

PROJECT TITLE:
ESTAFANOS HOUSE
DRAWING TITLE:
GENERAL NOTES

NAME: STEVEN ESTAFANOS
DATE: 25 JAN 2023
CLASS: ARC 8401-020
SCALE: NONE

A0.1

DOOR SCHEDULE

ID	FRAME C/W DOOR (W×H) (DOOR SIZE)	RSO (W×H)	QTY.	U.VAL.	COMMENTS
1	36"×80" (32"×78")	37"×81"	2	0.07	EXT STEEL INSULATED C/W IGU
2	26"×80" (24"×78")	27"×81"	1	N/A	HOLLOW CORE/SLAB
3	36"×80" UNIT PAIR	36"×80"	1	N/A	BYPASS SLIDER/SLAB
4	2-36"×83" C/W TRACK	32"×81"	2	N/A	SURFACE SLIDER

WINDOW SCHEDULE

ID	FRAME (W×H)	RSO (W×H)	QTY.	U.VAL.	COMMENTS (ALL UNITS ALUM. CLAD)
A	48"×36"	49"×37"	2	1.6	AWNING, BASEMENT
B	48"×96"-112" (SLOPED)	49"×97"-113" (SLOPED)	2	1.6	AWNING/FIXED
C	80"×80"	81"×81"	3	1.6	AWNING/FIXED
D	34"×80"	35"×81"	1	1.6	AWNING/FIXED
E	60"×18"	60"×19"	1	1.4	FIXED

NOTES:

1. DOORS & WINDOWS SHALL CONFORM TO REQUIREMENTS OF RESISTANCE TO FORCED ENTRY.


NO.	REVISION	DATE
1	FINAL SUBMISSION	12 APR 2023

PROJECT TITLE:
ESTAFANOS HOUSE

DRAWING TITLE:
DOOR SCHEDULE
WINDOW SCHEDULE


NAME: STEVEN ESTAFANOS
DATE: 15 FEB 2023
CLASS: ARC 8401 - 020
SCALE: NONE

A0.2

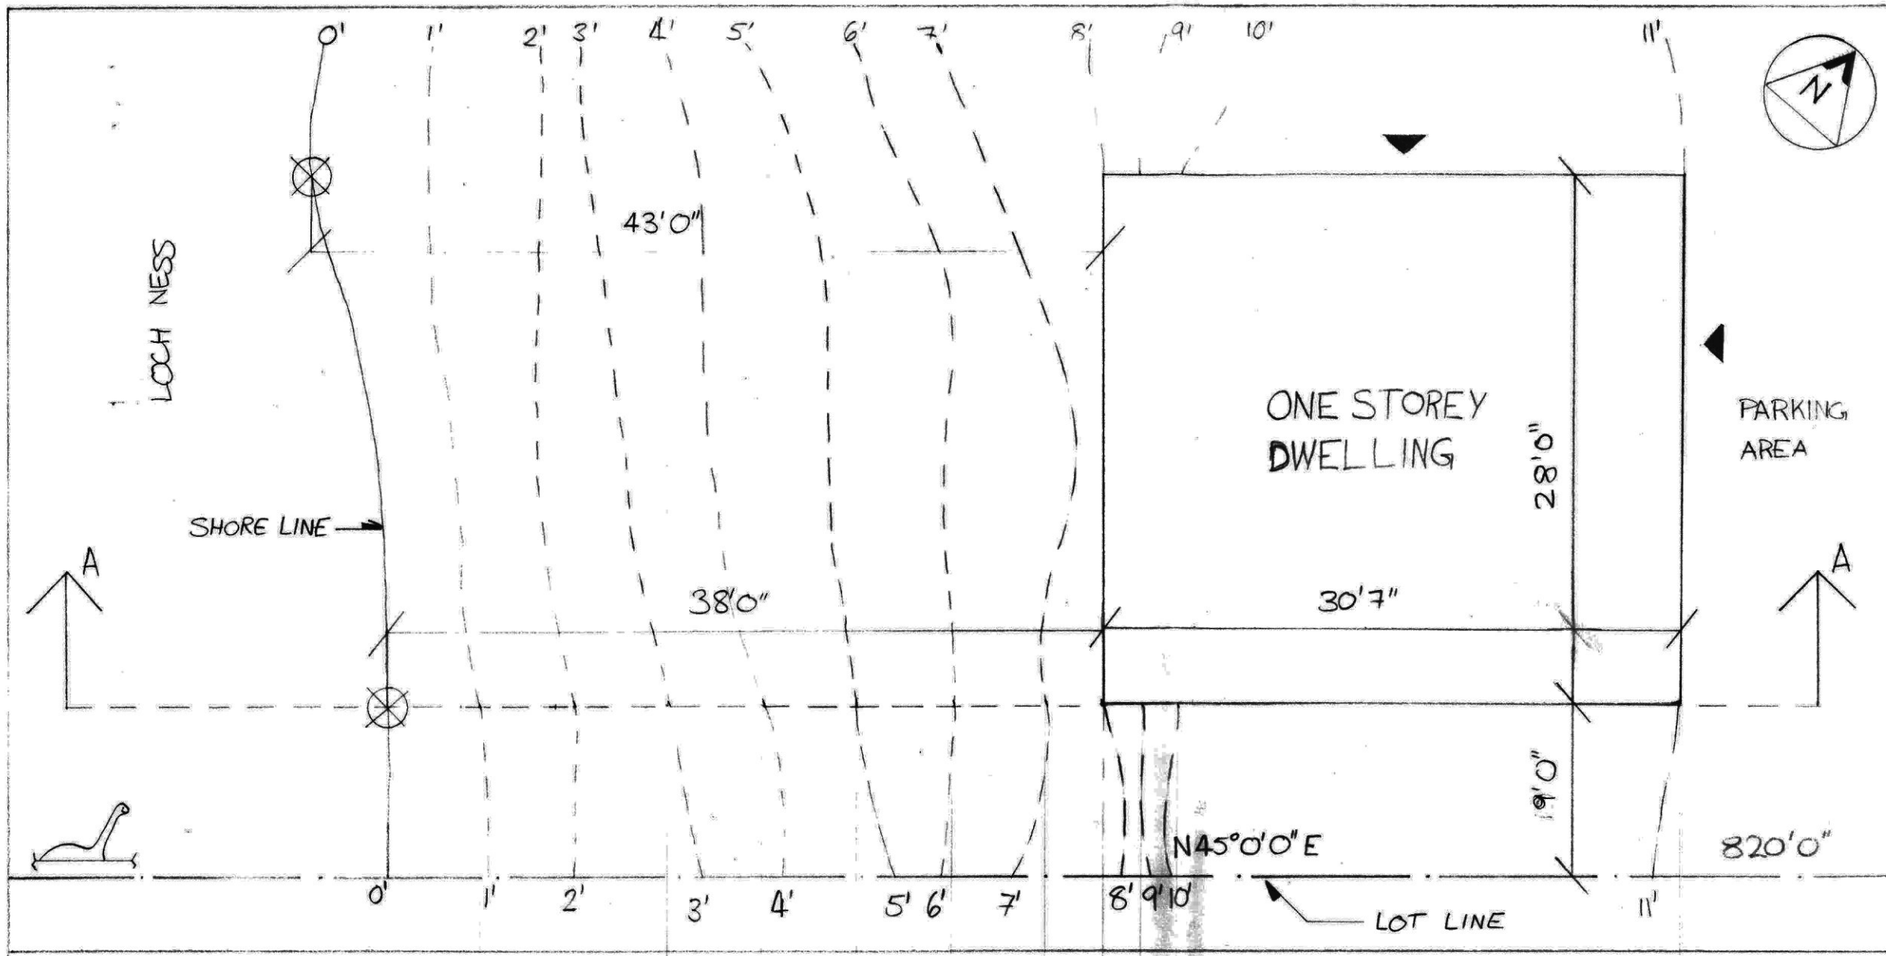

1 / A1.1 PARTIAL SITE PLAN

SCALE: 1/8" = 1'0"

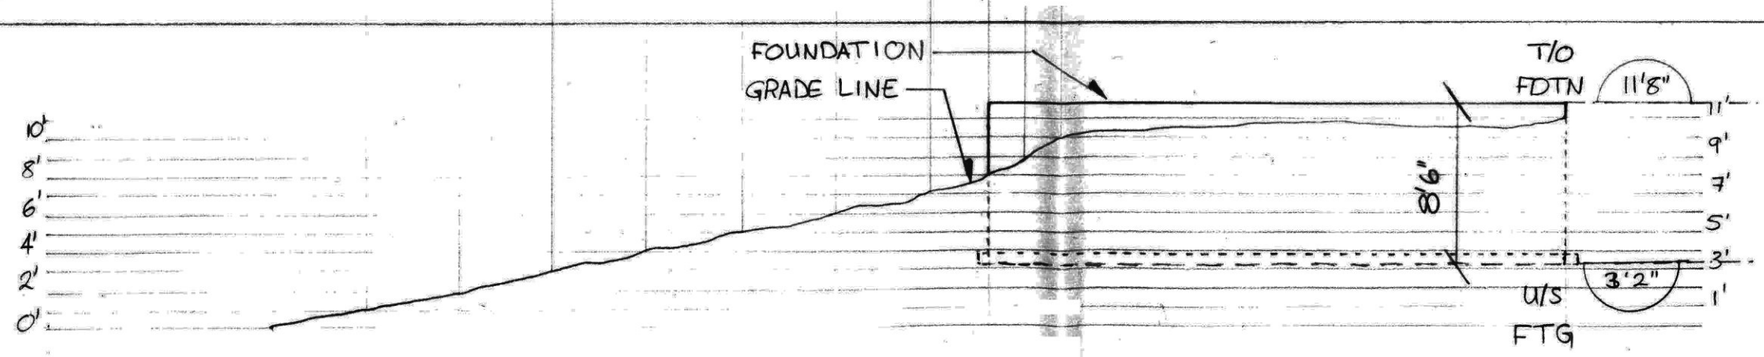

2 / A1.1 GRADE PROFILE A-A

SCALE: 1/8" = 1'0"

NOTES:

1. PARTIAL SITE/GRADE PLAN FOR GUEST HOUSE ONLY.
2. PROXIMITY OF BUILDING TO SHORELINE & SE PROPERTY LINE

LOT DESCRIPTION


PART LOT 12
PLAN 4M-1076

NO.	REVISION	DATE
1	FINAL SUBMISSION	12 APR 2023

PROJECT TITLE:
ESTAFANOS HOUSE
DRAWING TITLE:
SITE/GRADE PLAN

NAME: STEVEN ESTAFANOS
DATE: 15 FEB 2023
CLASS: ARC8401-020
SCALE: AS NOTED

A1.1

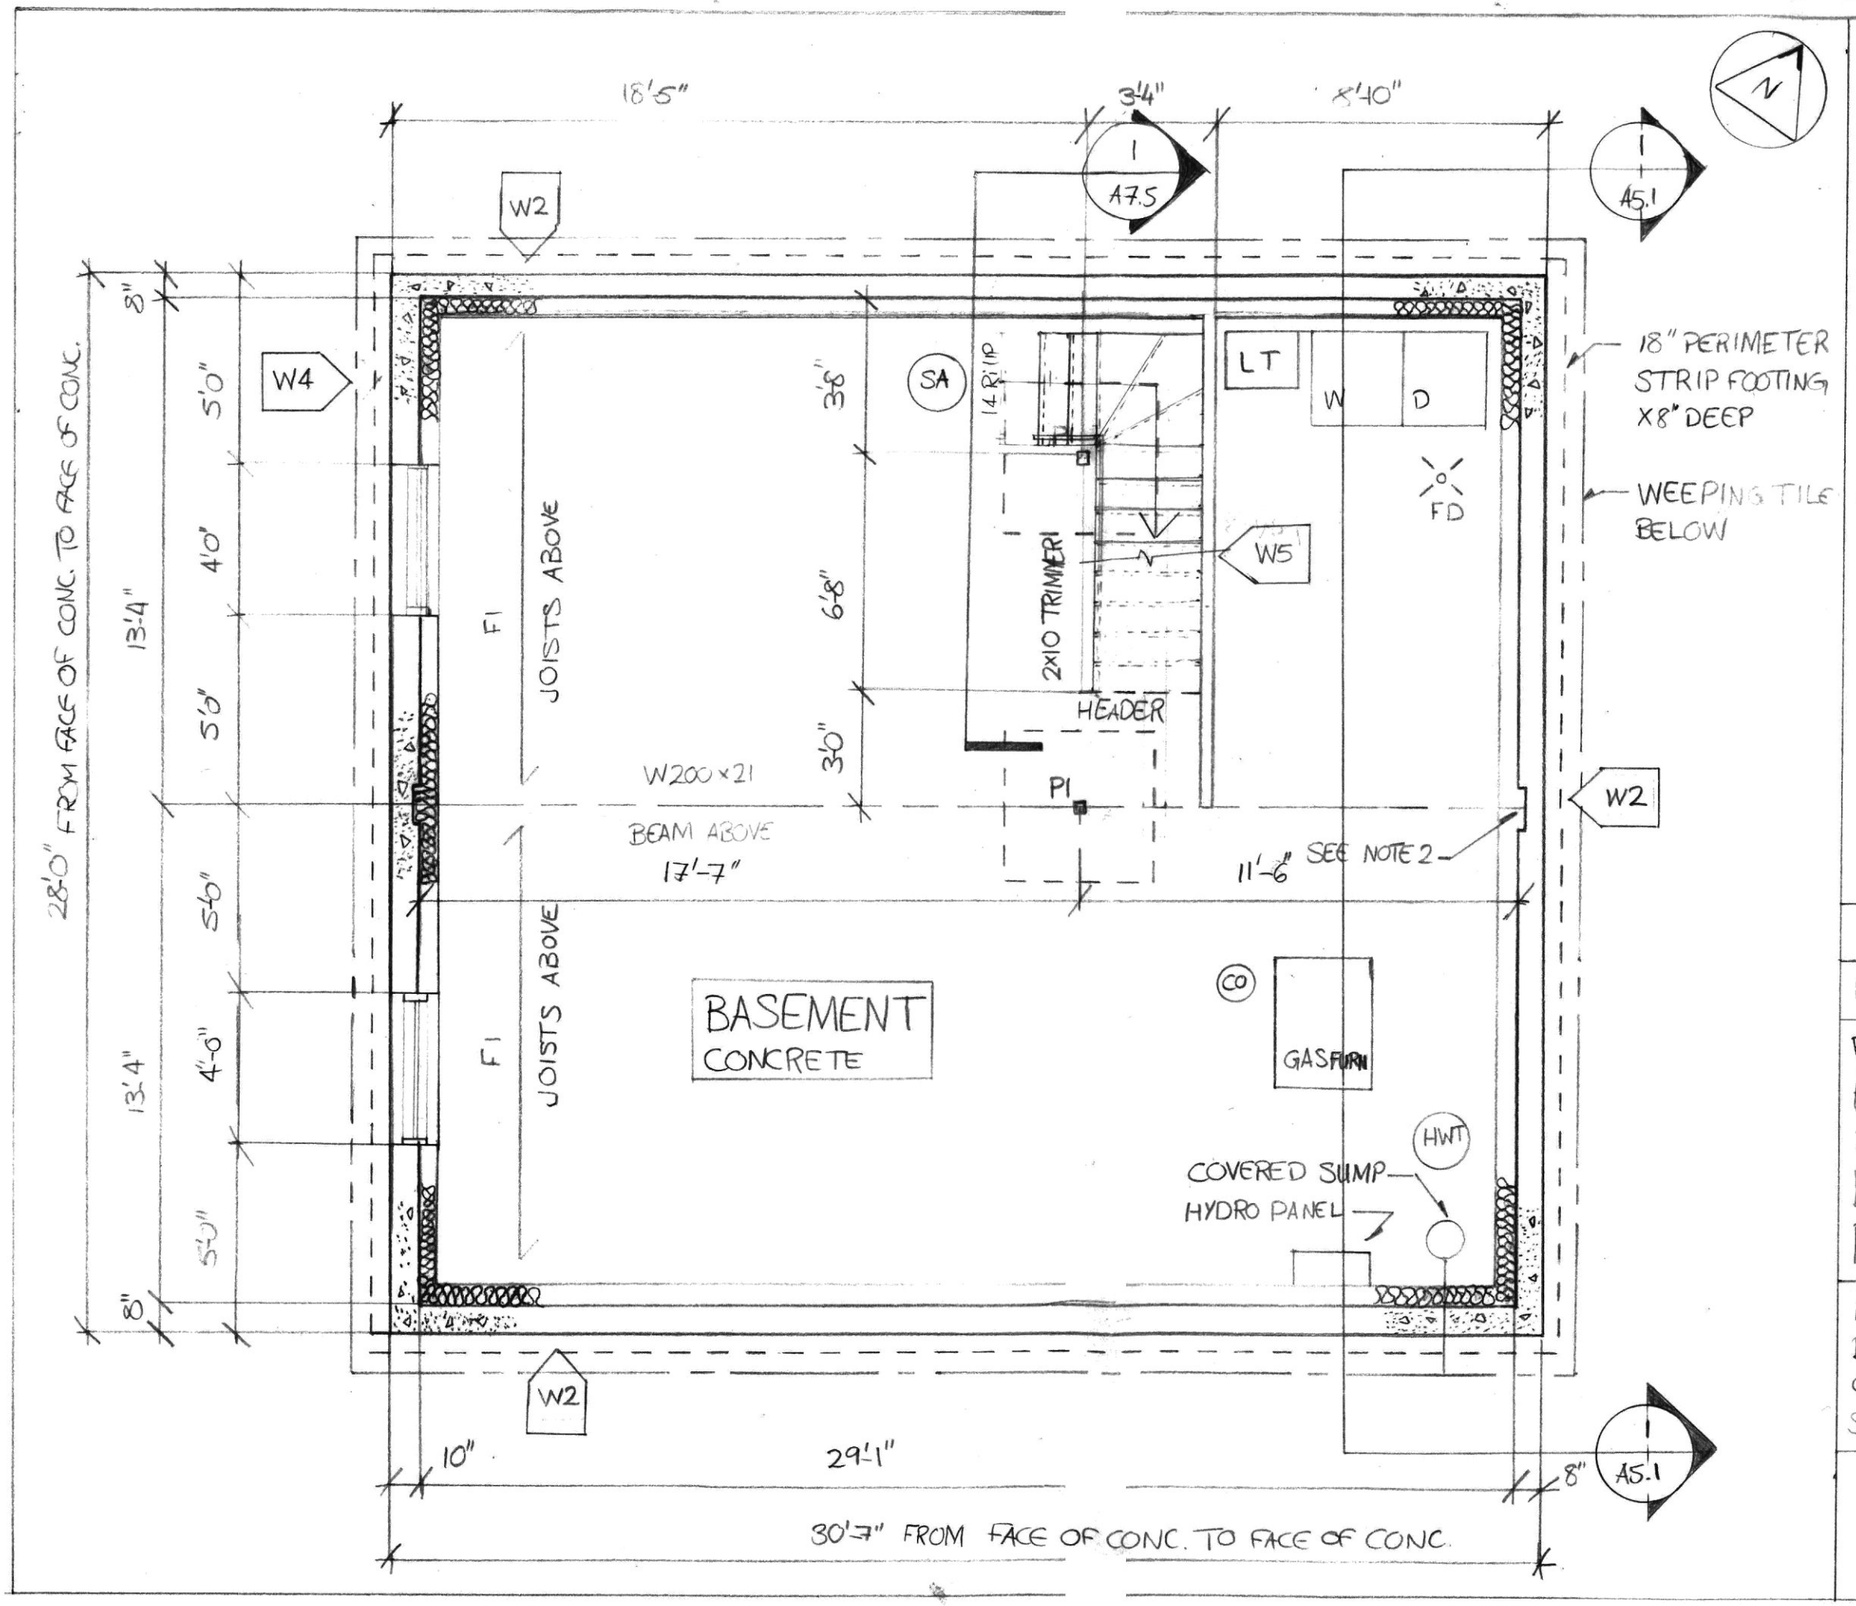

NOTES:

1. P1
   47"x47"x22" CONC. PAD
   3½"x3½"x3/16" HSS COLUMN
   C/W 6"x6"x5/8" BASE PLATES.
2. PROVIDE BEAM POCKETS.
   6"W x 4" DP x 8" H.
3. PROVIDE 2x4 @ 48" O/C BLOCKING AT ALL PARALLEL WALLS.
4. CONCRETE SLAB SLOPED TO DRAIN.


NO	REVISION	DATE
1	FINAL SUBMISSION	12 APR 2023

PROJECT TITLE:
ESTAFANOS HOUSE

DRAWING TITLE:
BASEMENT FLOOR PLAN

NAME: STEVEN ESTAFANOS
DATE: 8 FEB 2023
CLASS: ARC 8401-020
SCALE: 1/4" = 1'-0"

A2.1

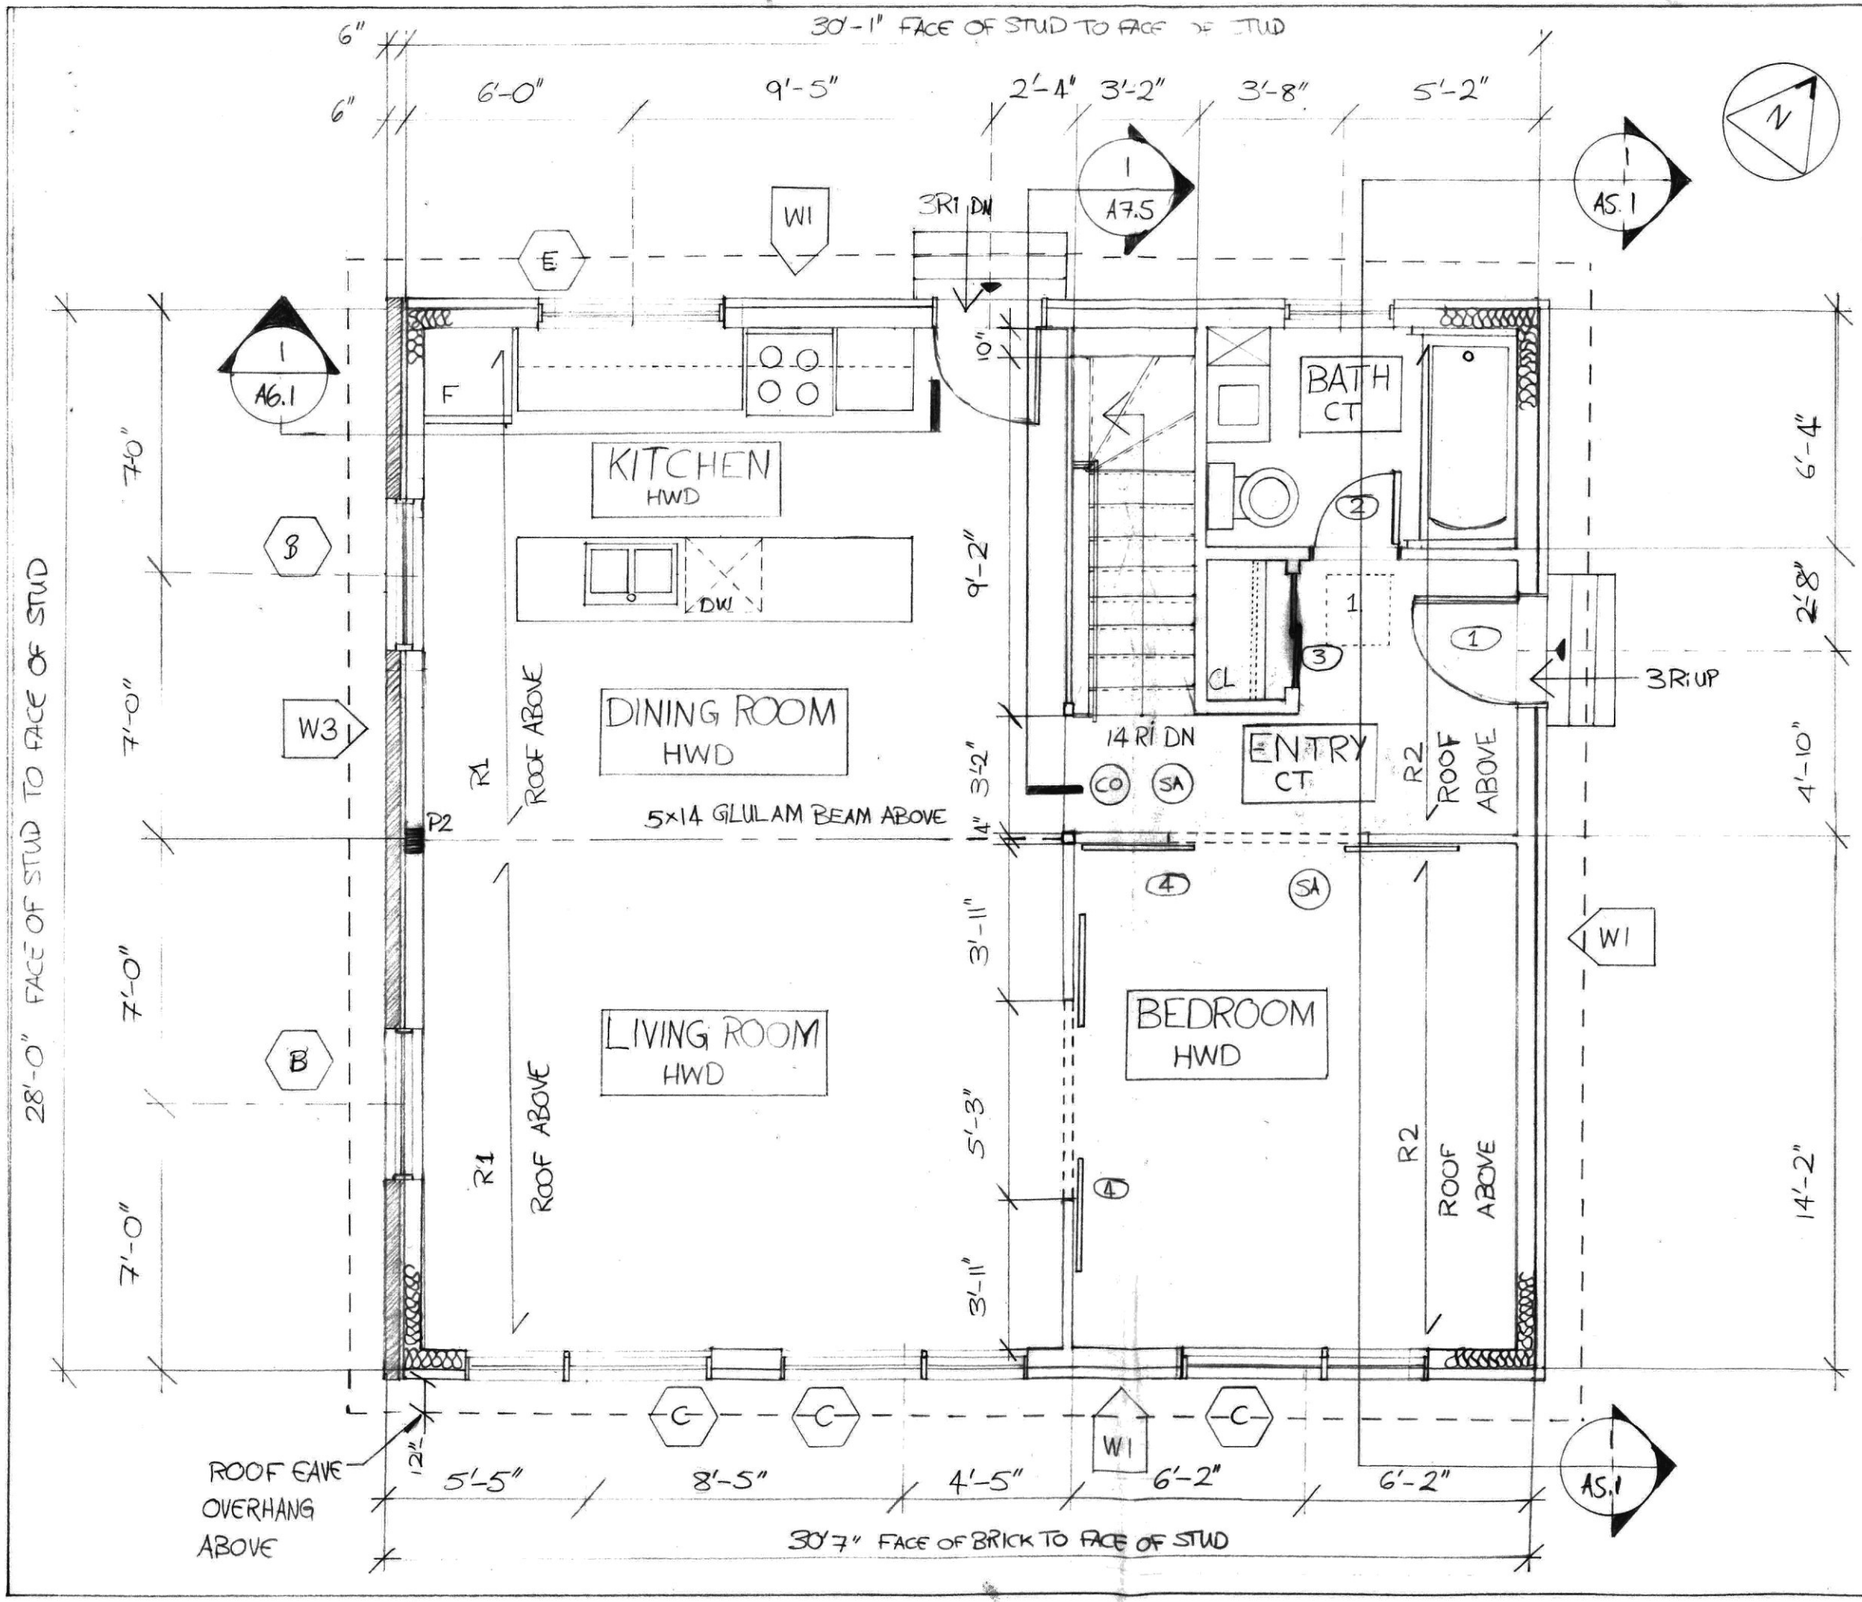

NOTES:

1. ATTIC ACCESS HATCH: 20" × 28"
2. P2: BUILT-UP POST: 5-2×6
   P3: GLULAM POST: 3½ × 3½
3. ALL LINTELS: 2×10


NO	REVISION	DATE
1	FINAL SUBMISSION	12 APR 2023

PROJECT TITLE:
ESTAFANOS HOUSE

DRAWING TITLE:
FIRST FLOOR PLAN

NAME: STEVEN ESTAFANOS
DATE: 22 FEB 2023
CLASS: ARC 8401-020
SCALE: 1/4" = 1'-0"

A2.2

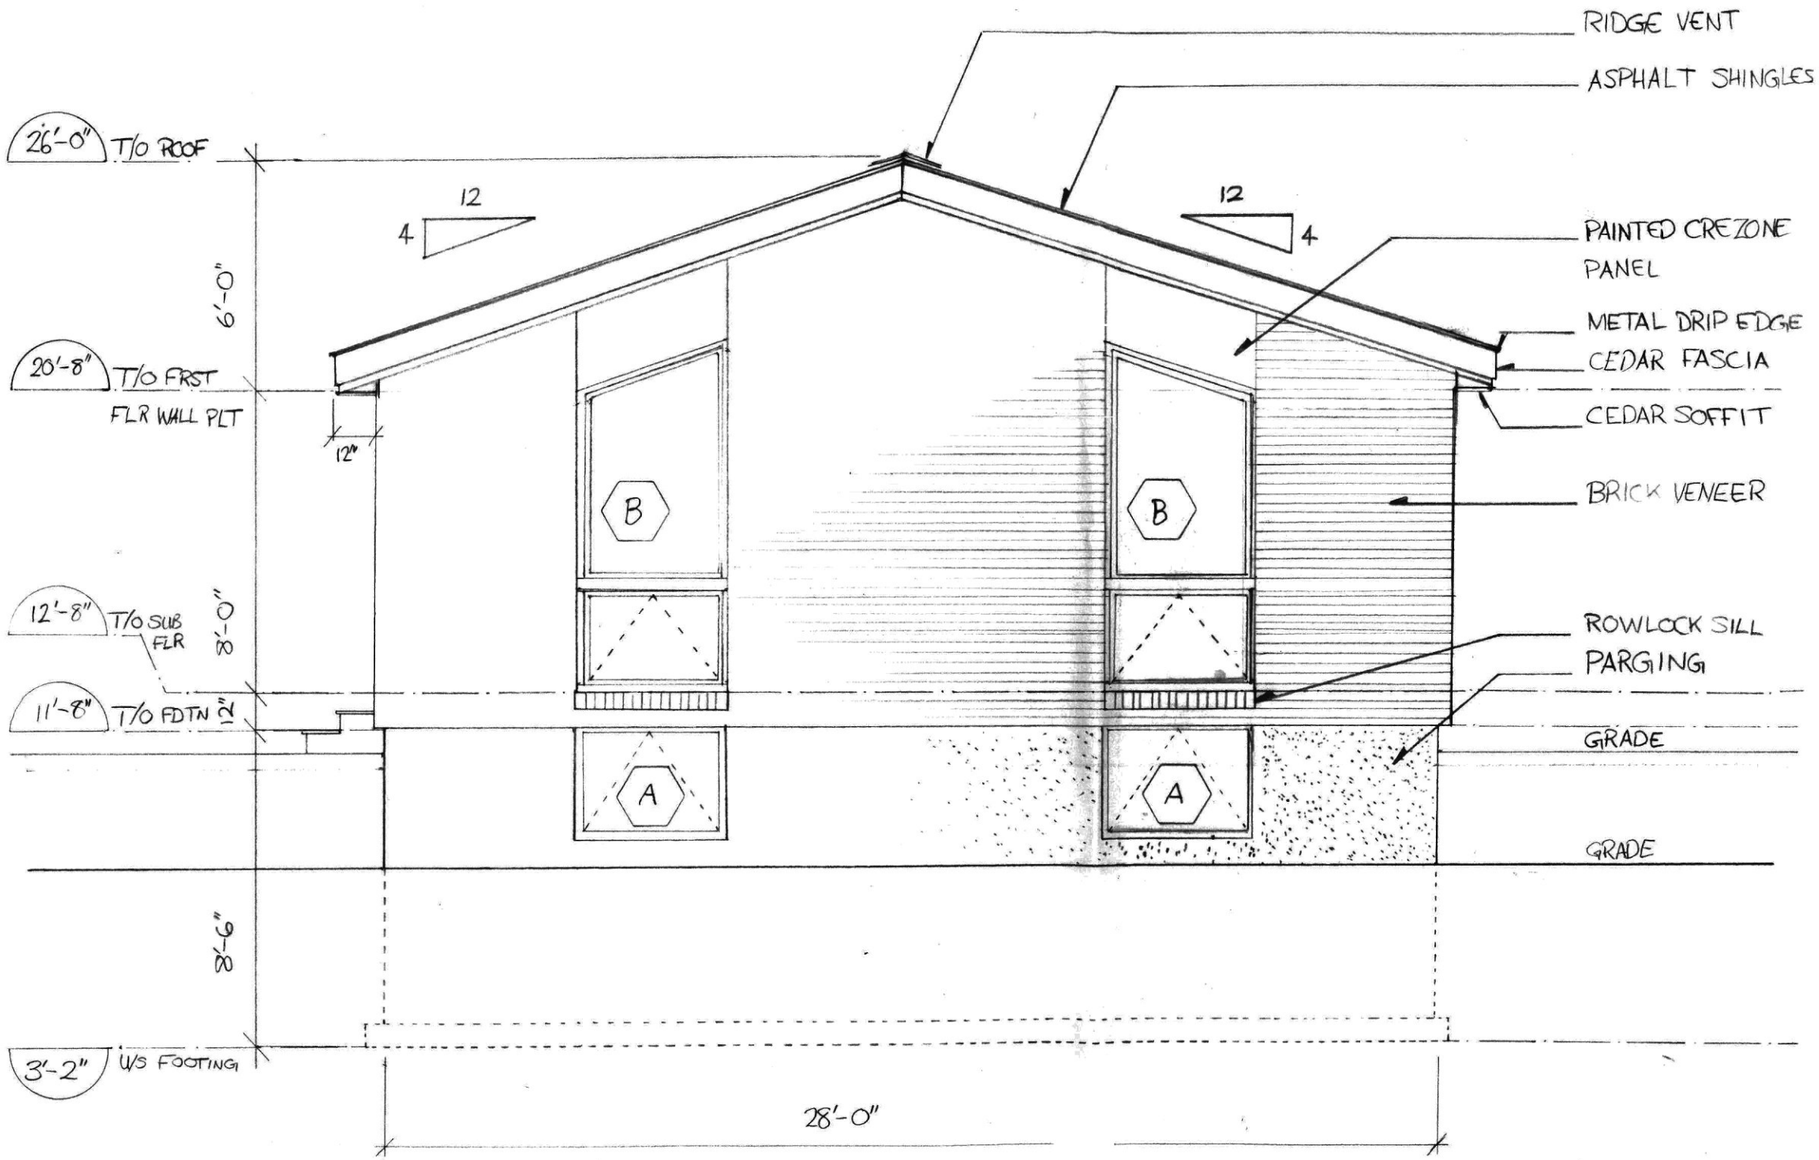

1 / A4.1 FRONT ELEVATION

SCALE: 1/4" = 1'-0"

NOTES:

1. 13'-10" AVERAGE GRADE TO MIDPOINT OF ROOF PITCH


NO	REVISION	DATE
1	FINAL SUBMISSION	12 APR 2023

PROJECT TITLE:
ESTAFANOS HOUSE

DRAWING TITLE:
FRONT ELEVATION

NAME: STEVEN ESTAFANOS
DATE: 22 MARCH 2023
CLASS: ARC 8401-020
SCALE: AS NOTED

A4.1

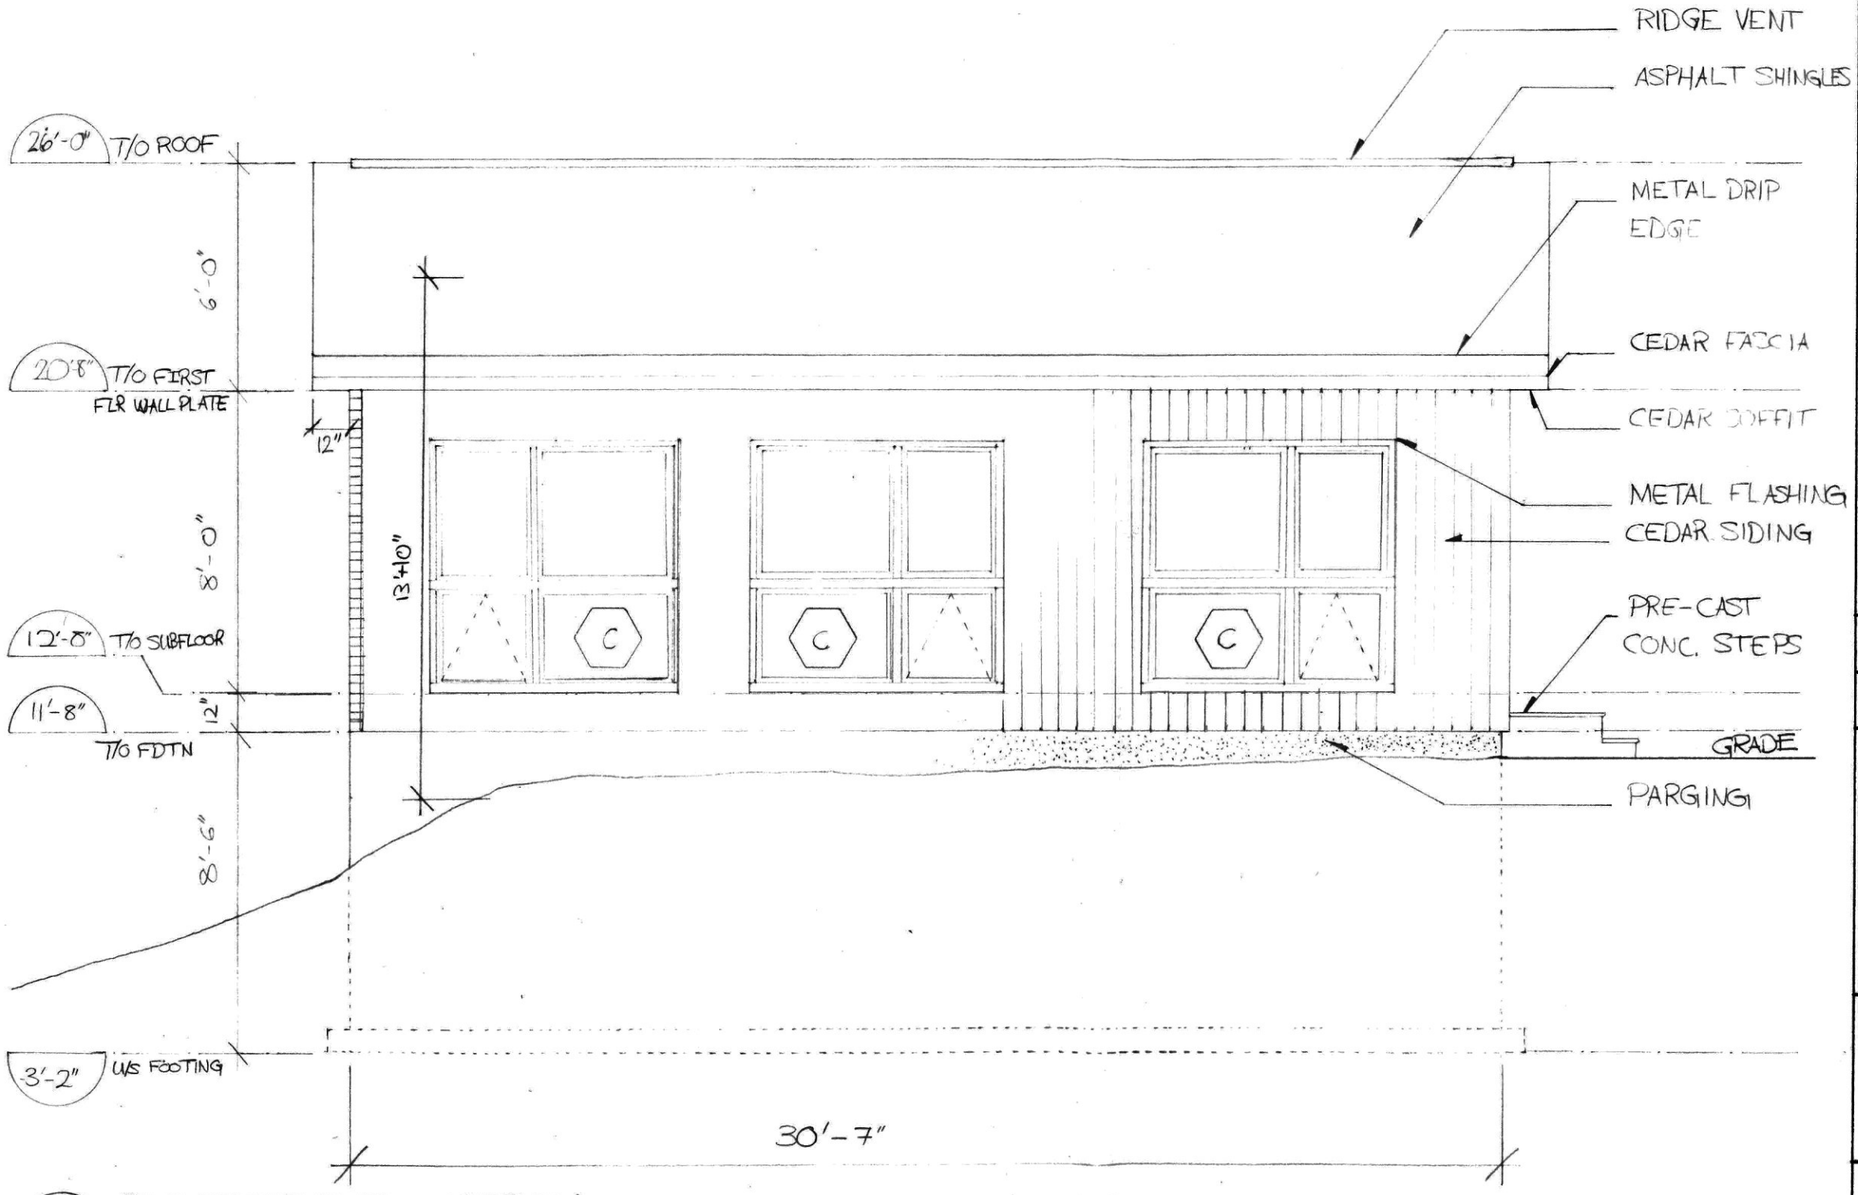

1 / A4.2 RIGHT SIDE ELEVATION

SCALE: 1/4" = 1'-0"

NOTES:


NO	REVISION	DATE
1	FINAL SUBMISSION	12 APR 2023

PROJECT TITLE:
ESTAFANOS HOUSE

DRAWING TITLE:
RIGHT SIDE ELEVATION

NAME: STEVEN ESTAFANOS
DATE: 22 MARCH 2023
CLASS: ARC-8401-020
SCALE: AS NOTED

A4.2

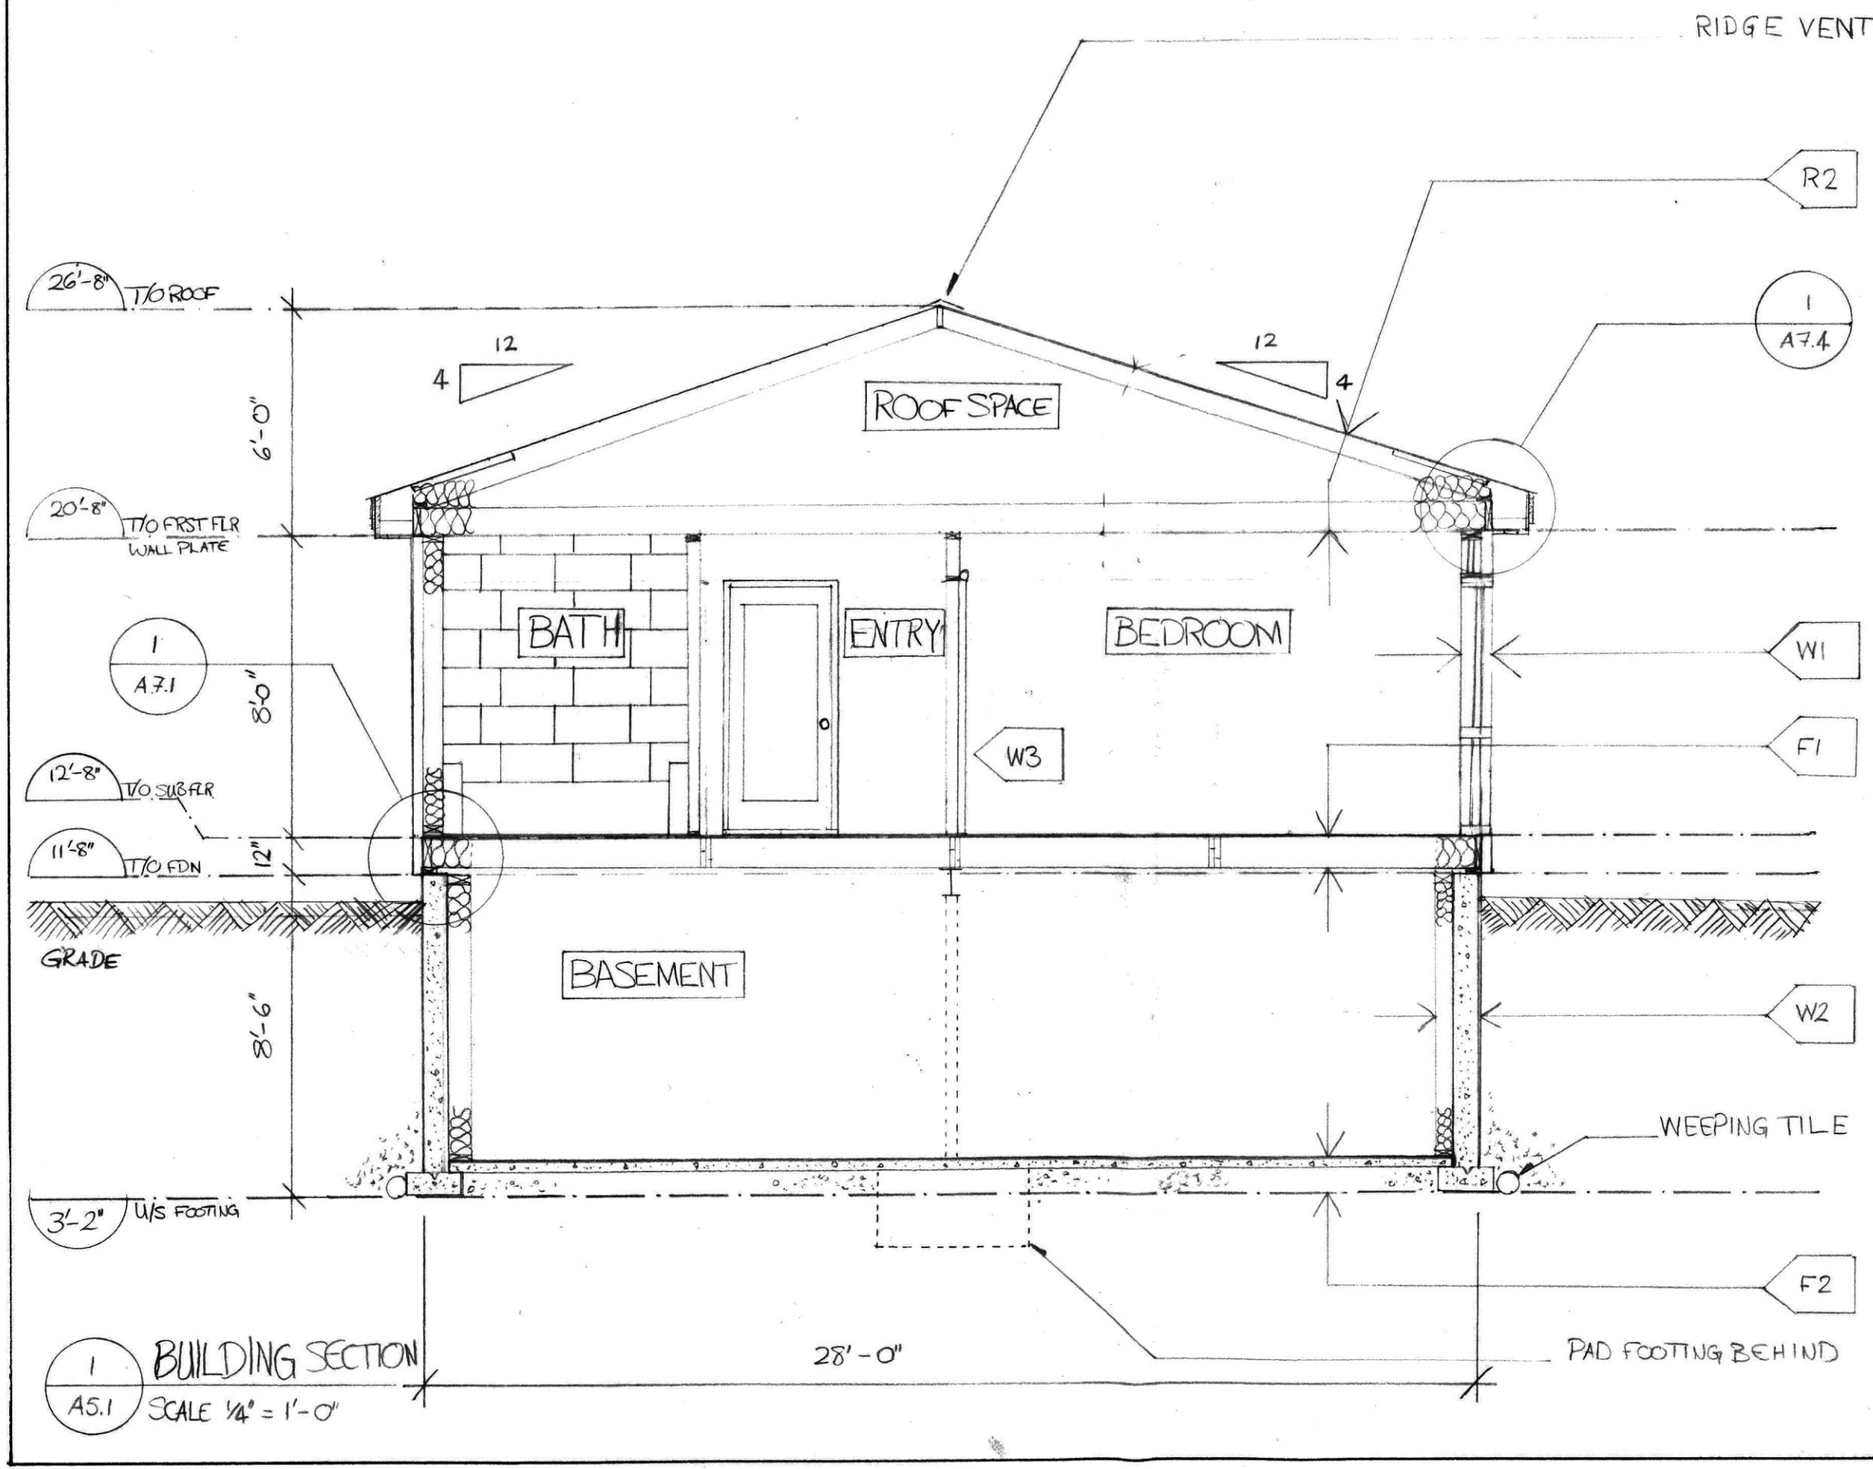

1 / A5.1 BUILDING SECTION
SCALE 1/4" = 1'-0"


NOTES:

NO	REVISION	DATE
1	FINAL SUBMISSION	12 APR 2023

PROJECT TITLE:
ESTAFANOS HOUSE
DRAWING TITLE:
BUILDING SECTION

NAME: STEVEN ESTAFANOS
DATE: 15 MARCH 2023
CLASS: ARC 8401-020
SCALE: AS NOTED

A5.1

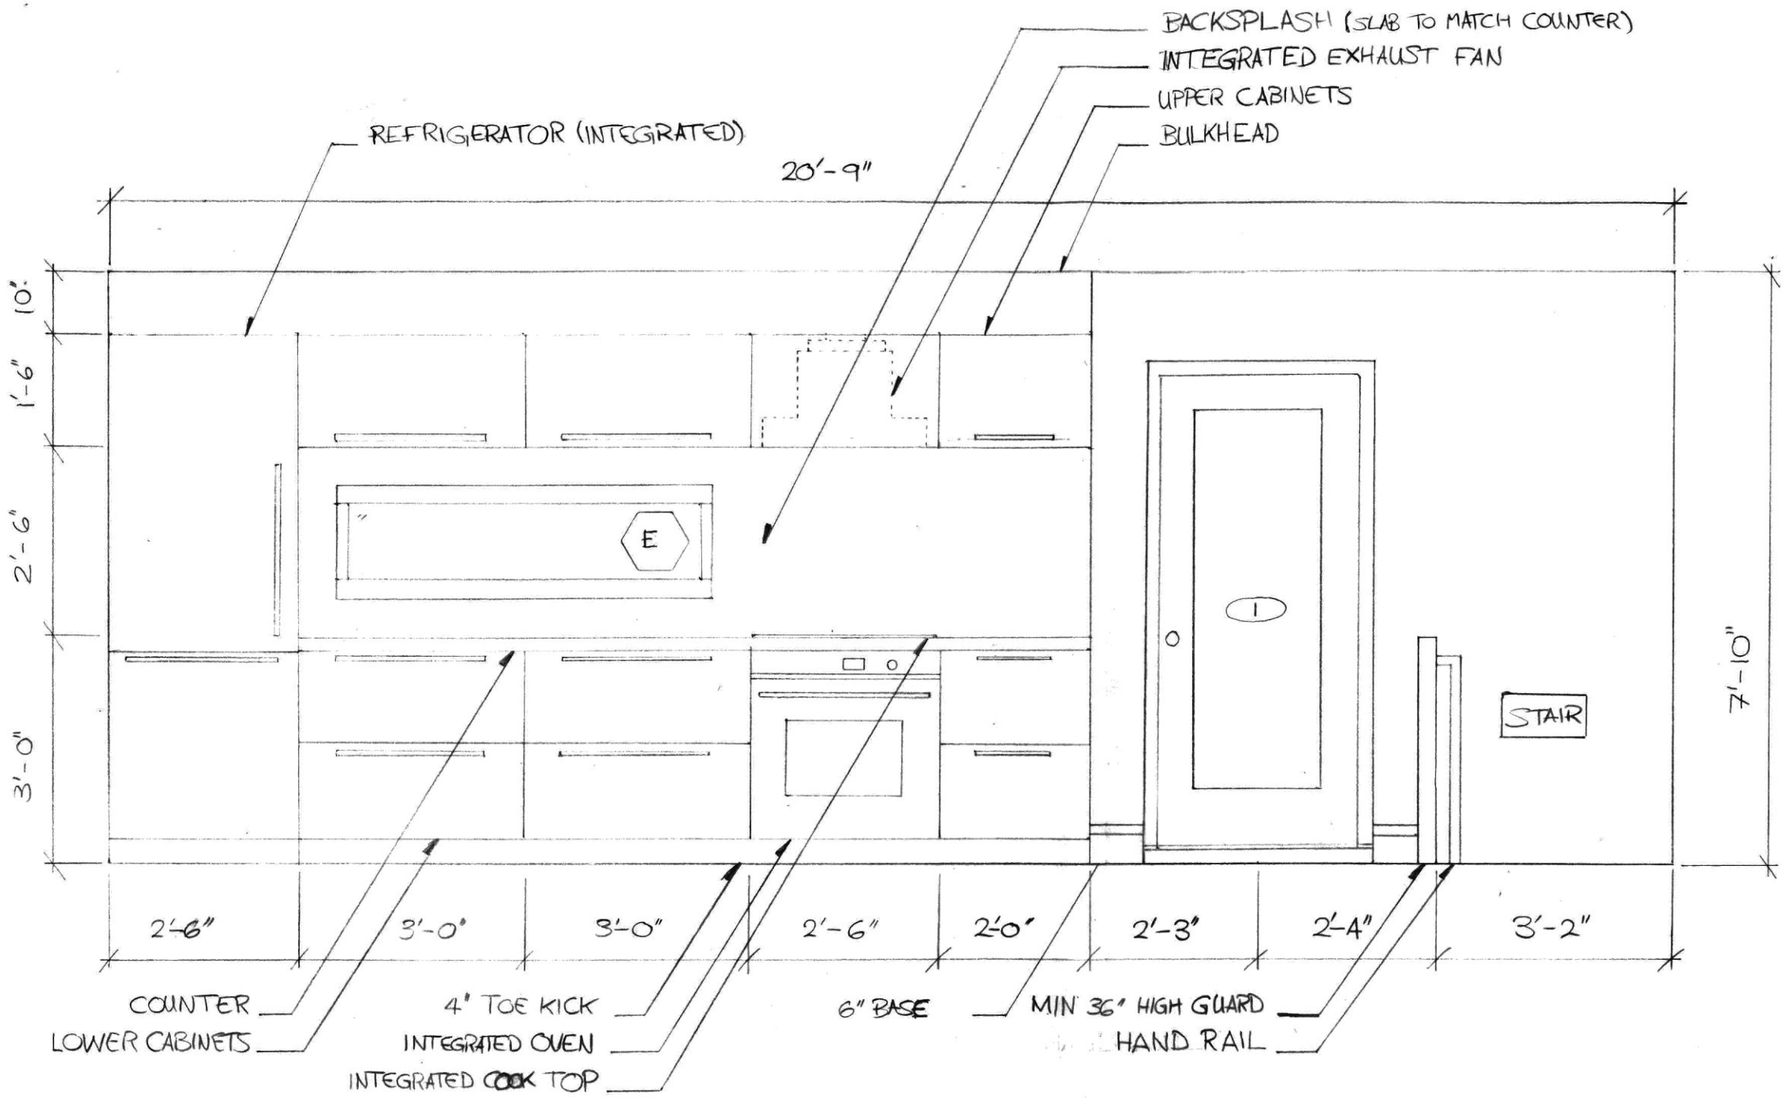

1 / A6.1 INTERIOR ELEVATION: KITCHEN

SCALE: ½" = 1'-0"

NOTES:

1. INTEGRATED REFRIGERATOR:
   FISHER & PAYKEL RS3084WRUK1
2. INTEGRATED OVEN:
   F&P OB30SDPTDB1
3. INTEGRATED COOK TOP:
   F&P C1304DTTB1
4. INTEGRATED EXHAUST FAN:
   F&P HPB3011-4_N


NO	REVISION	DATE
1	FINAL SUBMISSION	12 APR 2023

PROJECT TITLE:
ESTAFANOS HOUSE

DRAWING TITLE:
INTERIOR ELEVATION: KITCHEN

NAME: STEVEN ESTAFANOS
DATE: 5 APRIL 2023
CLASS: ARC 8401-020
SCALE: AS NOTED

A6.1

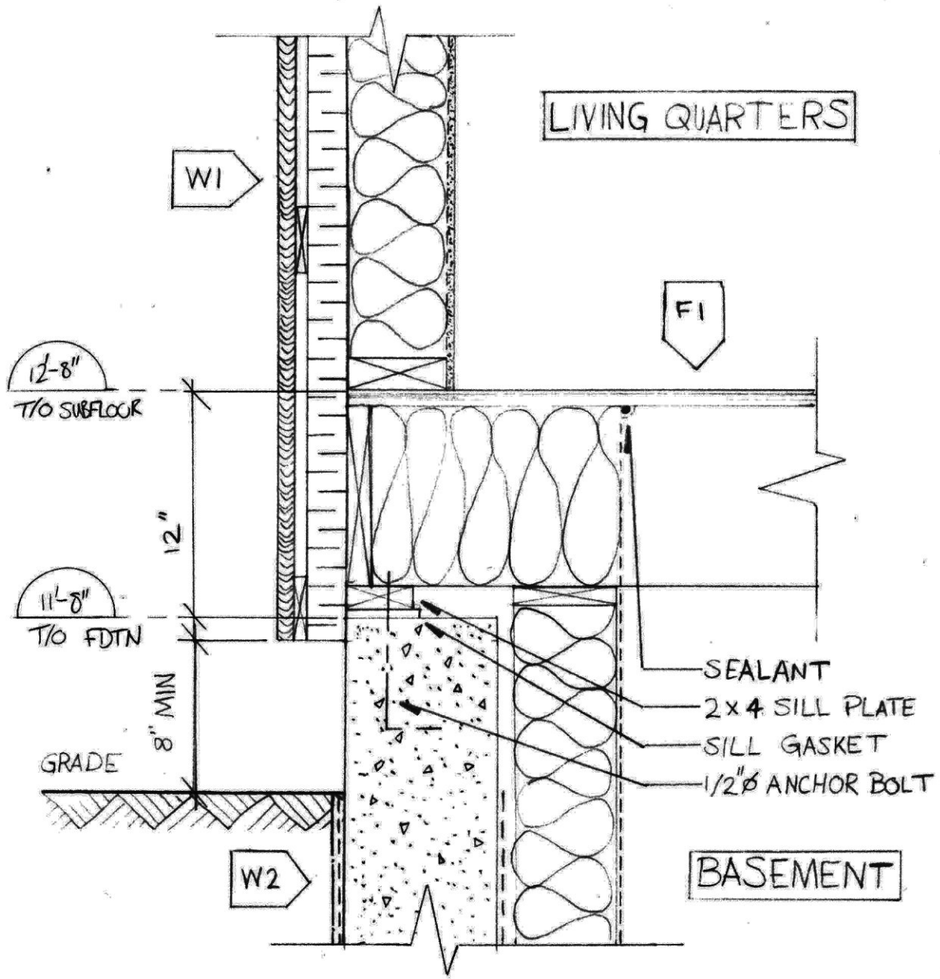

1 / A7.1 SILL DETAL 1
SCALE: 1 1/2" = 1"-0"


NOTES:

NO	REVISION	DATE
1	FINAL SUBMISSION	12 APR 2023

PROJECT TITLE:
ESTAFANOS HOUSE
DRAWING TITLE:
SILL DETAILS

NAME: STEVEN ESTAFANOS
DATE: 1 FEB 2023
CLASS: ARC 8401 - 020
SCALE: AS NOTED

A7.1

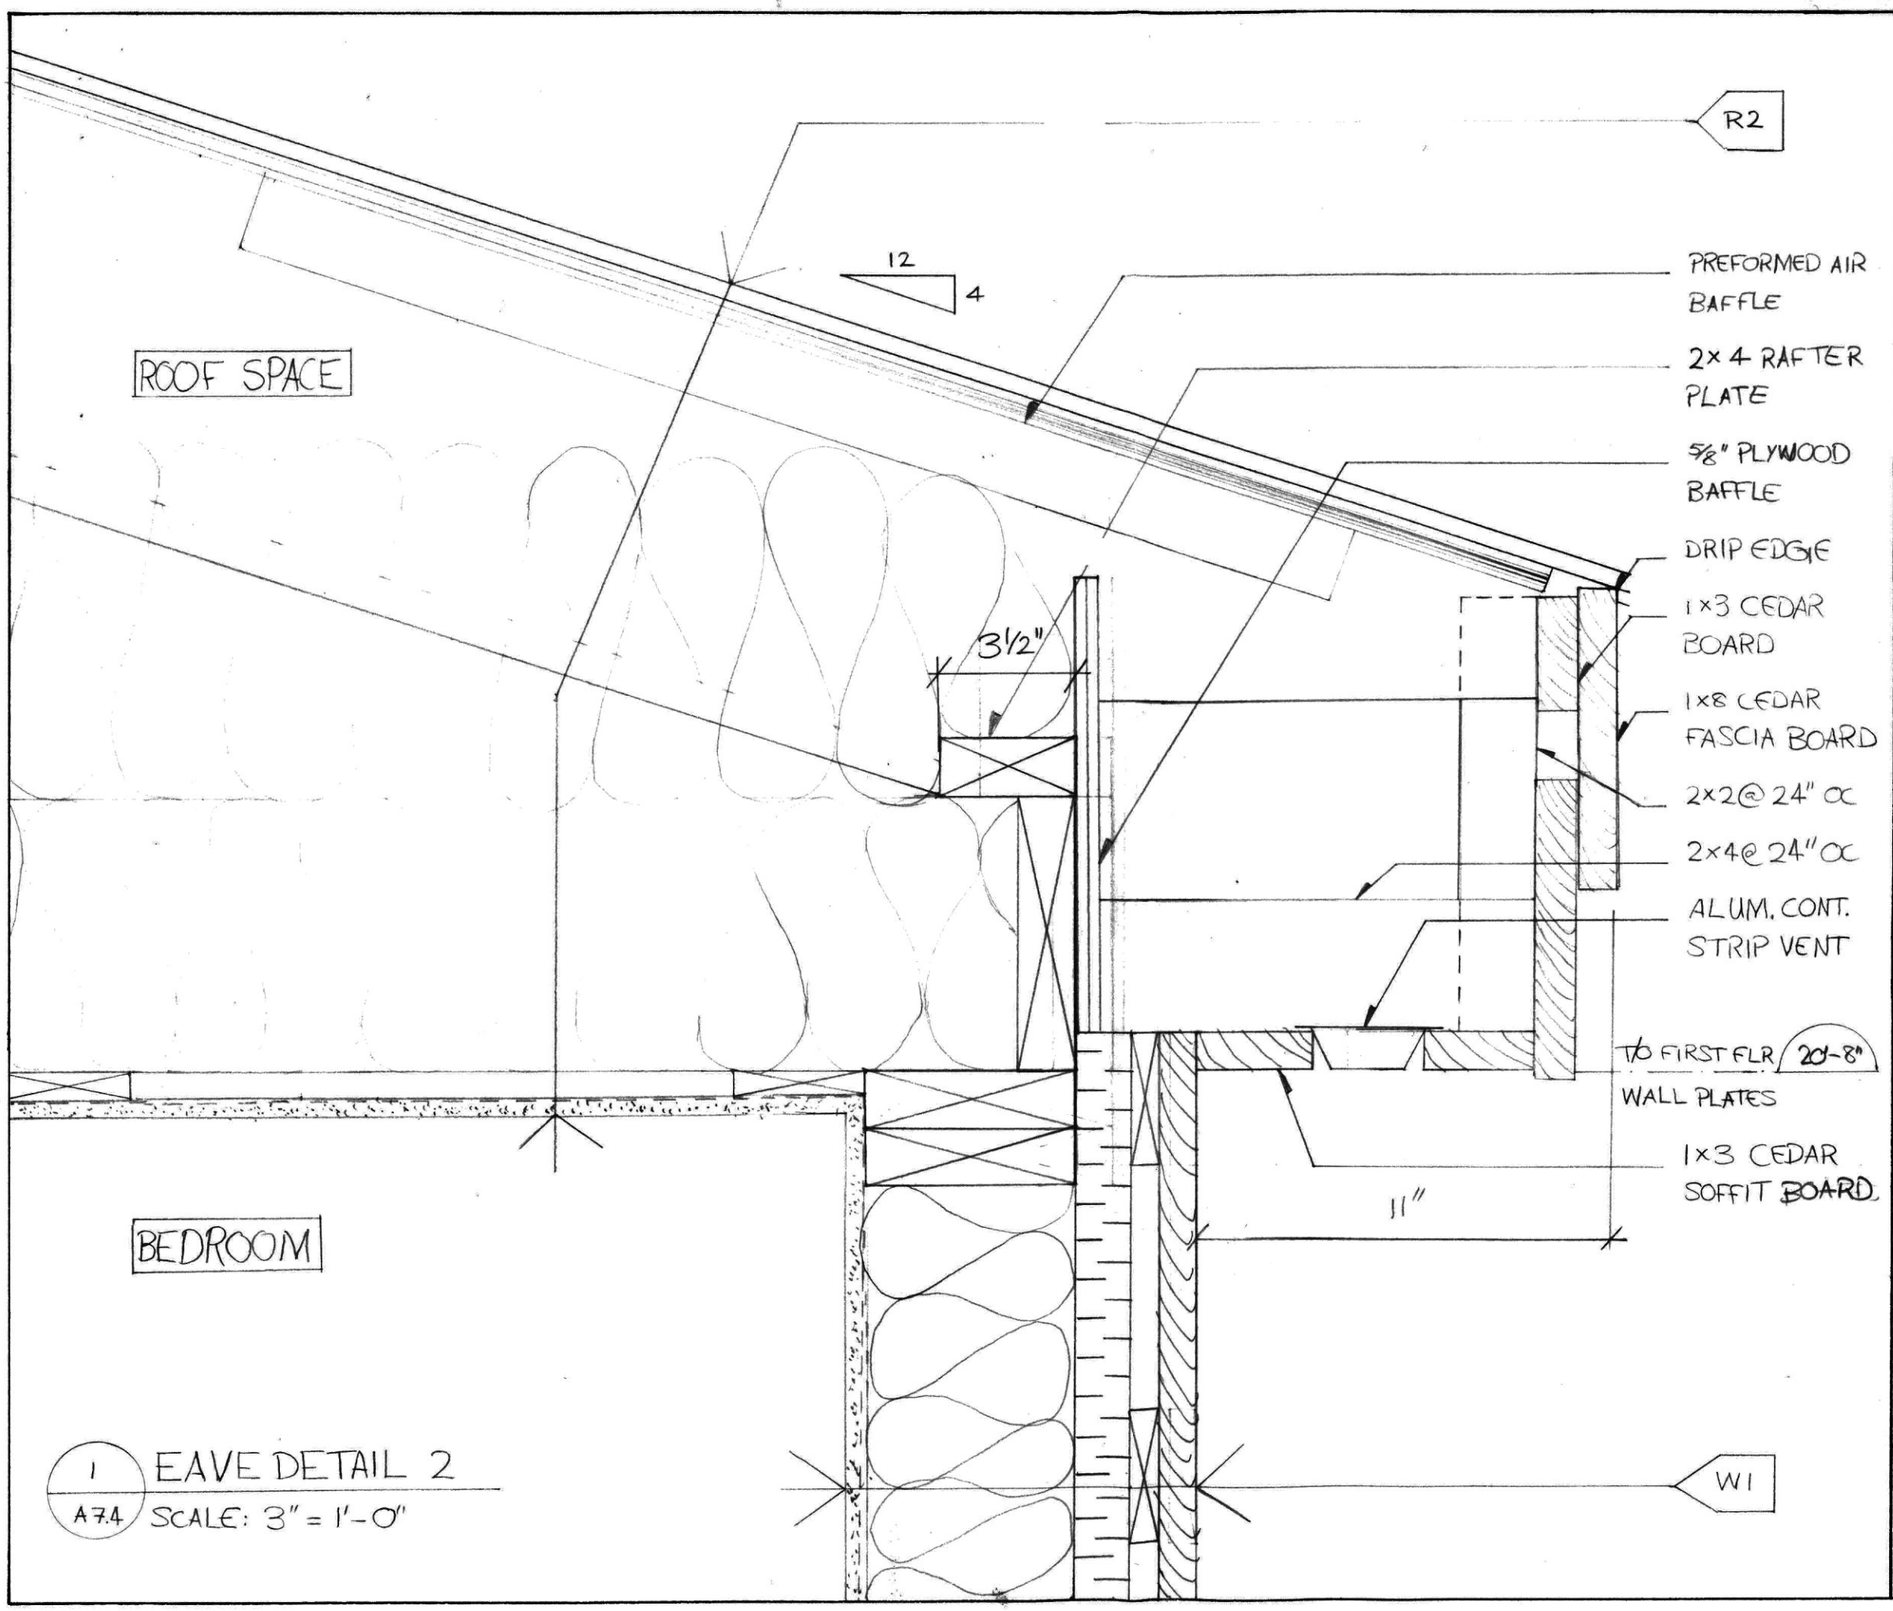

1 / A7.4 EAVE DETAIL 2
SCALE: 3" = 1'-0"

NOTES


NO	REVISION	DATE
1	~~FINAL~~ SUBMISSION	12 APR 2023

PROJECT TITLE:
ESTAFANOS HOUSE

DRAWING TITLE:
EAVE DETAIL 2


NAME: STEVEN ESTAFANOS
DATE: 8 MAR 2023
CLASS: ARC 8401-020
SCALE: AS NOTED

A7.4

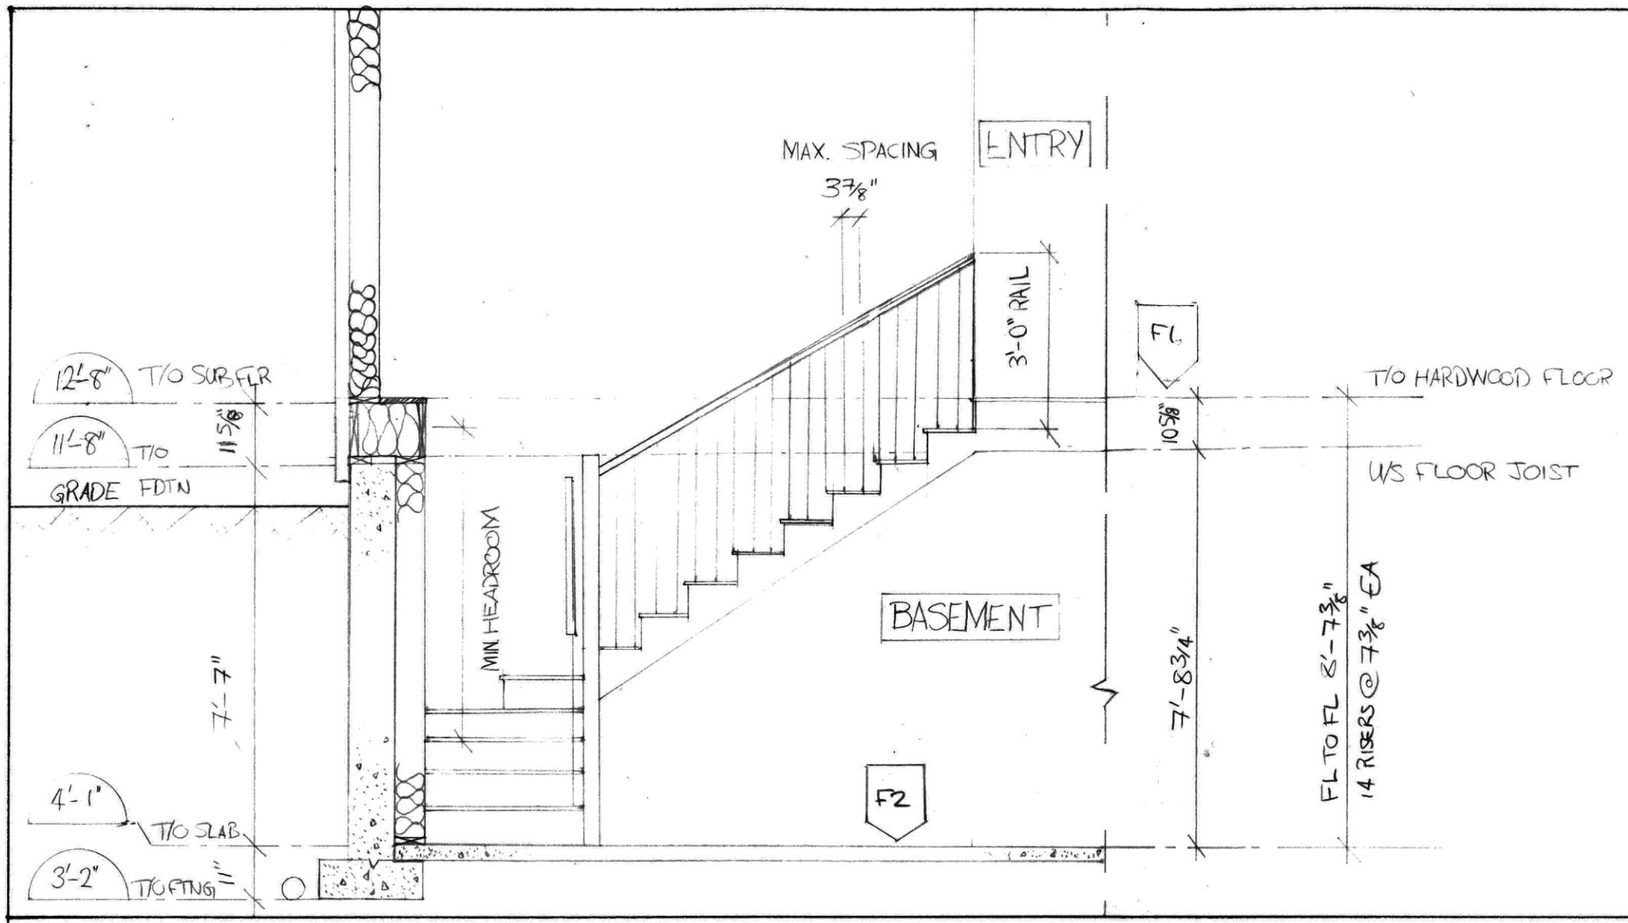

1 / A7.5 STAIR ELEVATION/WALL SECTION

SCALE: 3/8" = 1'-0"

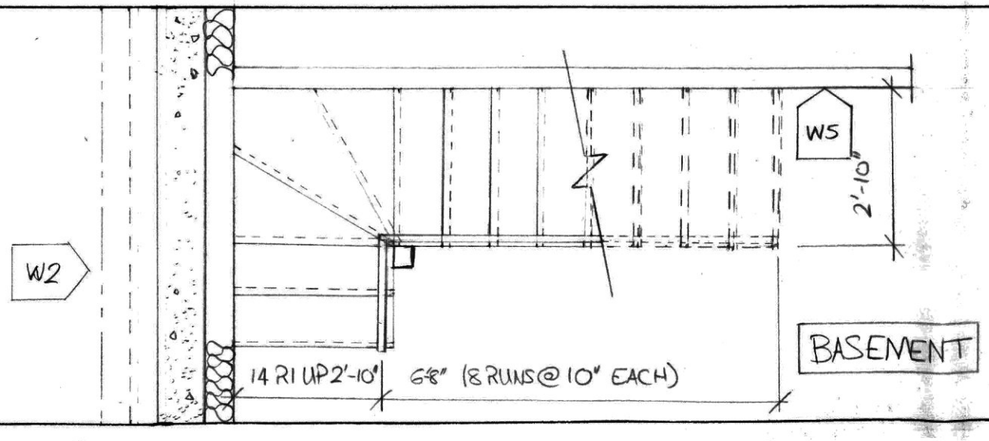

2 / A7.5 BASEMENT STAIR PLAN (ROTATED)

SCALE: 3/8" = 1-0"

NOTES:

TOTAL RISE =
14 RISERS @ 7
13 STEPS:
- 8 RUNS @ 10" DEEP EA
- 3 WINDERS @ 30°
- 2 RUNS @ 10" DEEP EA

NOSINGS = 1" EA (TREAD - 11")
HEADROOM =
HANDRAILS 3'-0" HIGH
GUARD ABOVE 3'-0" HIGH
STRINGER - 2X12

NO	REVISION	DATE
1	FINAL SUBMISSION	12 APR 2023

PROJECT TITLE:
ESTAFANOS HOUSE
DRAWING TITLE:
STAIR DETAILS

NAME: STEVEN ESTAFANOS
DATE: 29 MARCH 2023
CLASS: ARC-8401-020
SCALE: AS NOTED

A7.5